




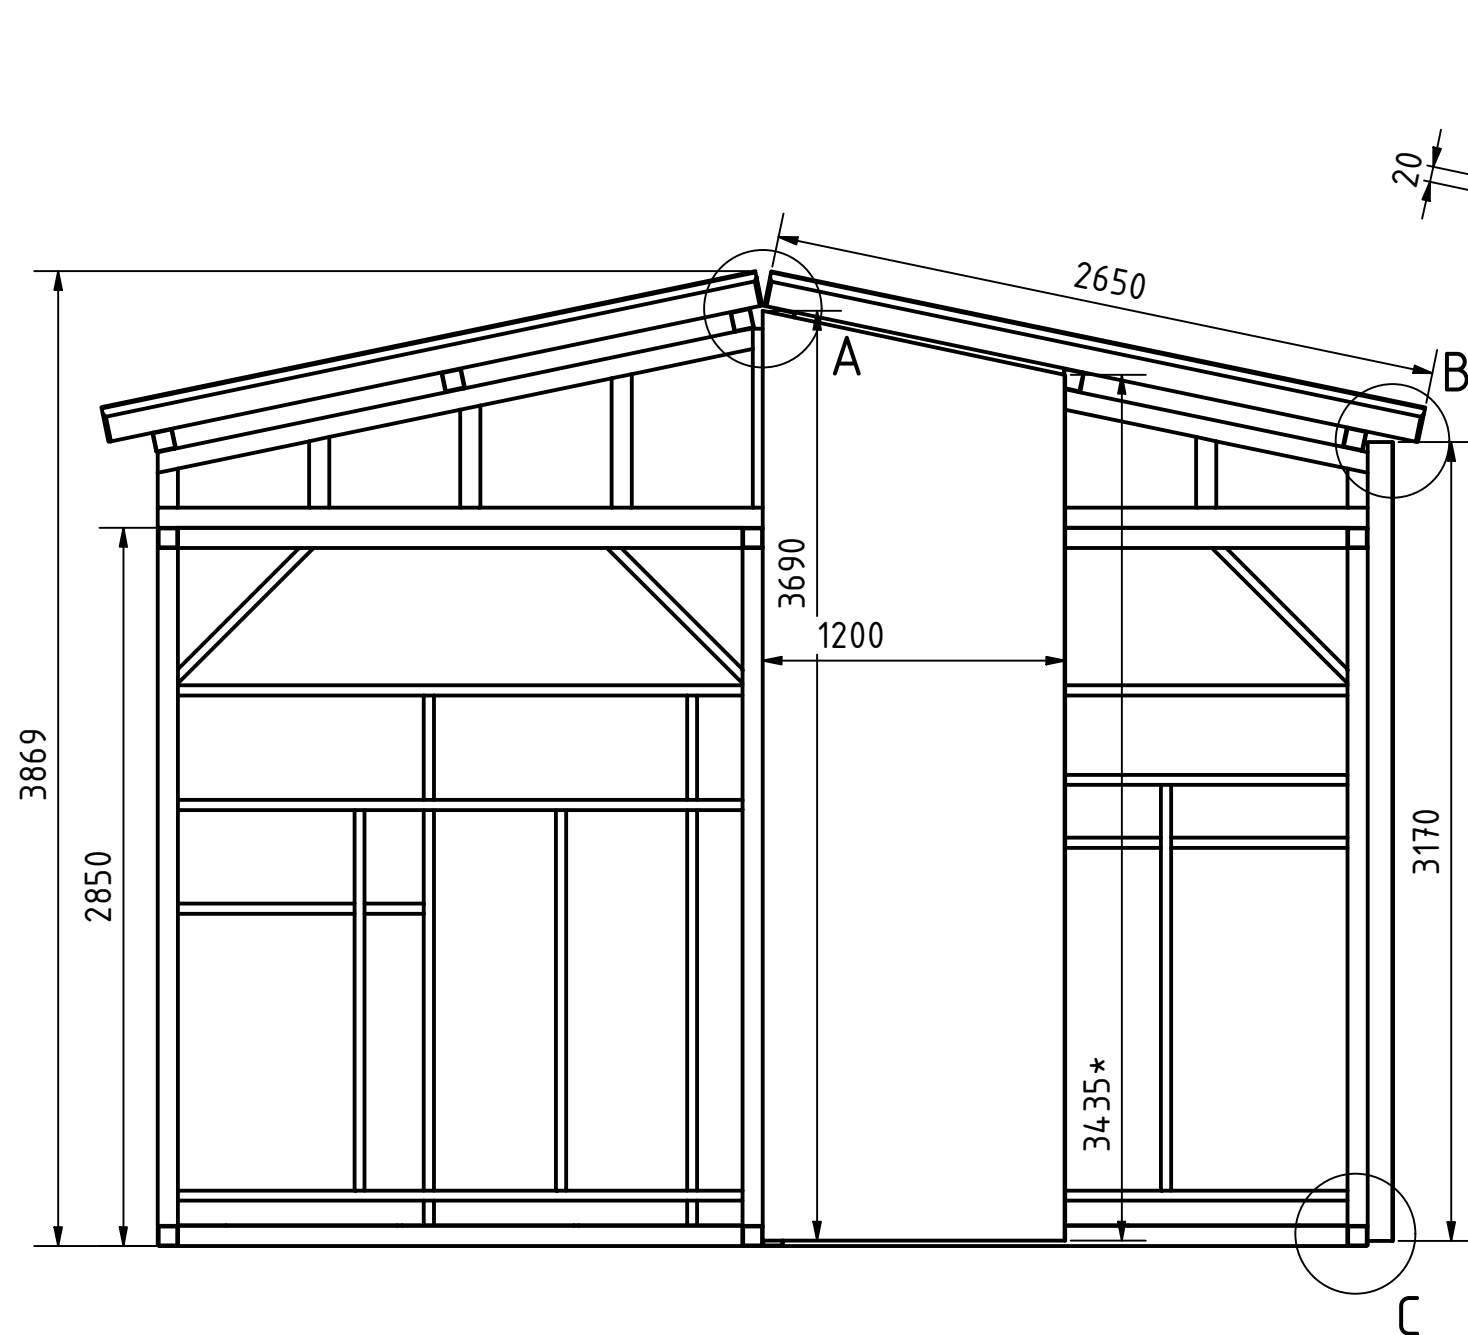

A (1 : 10)

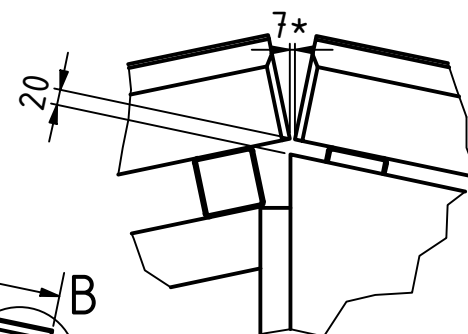

B (1 : 10)

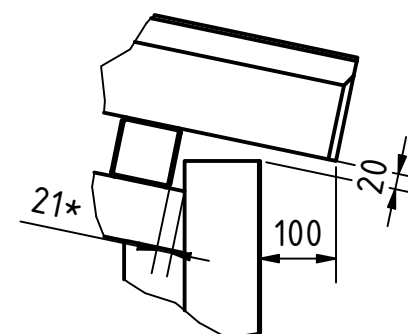

C (1 : 10)

