

**ОБЩЕСТВО С ОГРАНИЧЕННОЙ ОТВЕТСТВЕННОСТЬЮ
«МСБ»**

ОГРН 1107847144074

ИНН 7814467781 КПП 784201001

**191144, г. Санкт-Петербург, ул. Новгородская, д. 14, лит. А
рас.счет 40702 810 4 9033 000213 в ПАО «БАНК «САНКТ-ПЕТЕРБУРГ»
кор.счет 30101 810 9 0000 0000790 БИК 044030790**

№ СРО-П-179-12122012

СРО

14192.016/2025-СПОЗУ

обозначение тома

РАБОЧАЯ ДОКУМЕНТАЦИЯ

Модернизация объекта «Здание: Стационарные очистные сооружения» в с. Са-
лемал»

наименование проектируемого предприятия

Схема планировочной организации земельного участка

наименование комплекта

Изм.	№ док.	Подп.	Дата

Санкт-Петербург
2025 год

ОБЩЕСТВО С ОГРАНИЧЕННОЙ ОТВЕТСТВЕННОСТЬЮ

«МСБ»

ОГРН 1107847144074

ИНН 7814467781 КПП 784201001

**191144, г. Санкт-Петербург, ул. Новгородская, д. 14, лит. А
рас.счет 40702 810 4 9033 000213 в ПАО «БАНК «САНКТ-ПЕТЕРБУРГ»
кор.счет 30101 810 9 0000 0000790 БИК 044030790**

№ СРО-П-179-12122012

СРО

14192.016/2025-СПОЗУ

обозначение тома

РАБОЧАЯ ДОКУМЕНТАЦИЯ

Модернизация объекта «Здание: Стационарные очистные сооружения» в с.
Салемал»

наименование проектируемого предприятия

Схема планировочной организации земельного участка

наименование комплекта

Генеральный директор

А.Ю. Кирдис

Главный инженер проекта

С.А. Усвятцев

Санкт-Петербург
2025 год

Содержание раздела

Обозначение	Наименование	Страница	Примечание
14192.016/2025 - СПОЗУ. СТ	Содержание тома	2	
14192.016/2025 -СП	Состав проектной документации		
14192.016/2025 - СПОЗУ. ТЧ	Текстовая часть	4	
	а) характеристика земельного участка, предоставленного для размещения объекта капитального строительства	4	
	б) обоснование границ санитарно-защитных зон объектов капитального строительства в пределах границ земельного участка - в случае необходимости определения указанных зон в соответствии с законодательством Российской Федерации	5	
	в) обоснование и описание планировочной организации земельного участка в соответствии с градостроительным и техническим регламентами либо документами об использовании земельного участка (если на земельный участок не распространяется действие градостроительного регламента или в отношении его не устанавливается градостроительный регламент)	5	
	г) технико-экономические показатели земельного участка, предоставленного для размещения объекта капитального строительства	6	
	д) обоснование и описание решений по инженерной подготовке территории, в том числе решений по инженерной защите территории и объектов капитального строительства от последствий опасных геологических процессов, паводковых, поверхностных и грунтовых вод	6	
	е) организация рельефа вертикальной планировкой	6	
	ж) описание решений по благоустройству территории	6	
	з) обоснование зонирования территории земельного участка, предоставленного для размещения объекта капитального строительства, обоснование функционального назначения и принципиальной схемы размещения зон, обоснование размещения зданий и сооружений	7	

						10.25	14192.016/2025-СПОЗУ			
Изм.	Кол.уч.	Лист	№ док.	Подп.	Дата			Стадия	Лист	Листов
Разработал	Мульдьяров				10.25			П	1	2
Пров.	Петрова				10.25					
ГИП	Петрова				10.25		Содержание			ООО «МСБ»

	(основного, вспомогательного, подсобного, складского и обслуживающего назначения) объектов капитального строительства - для объектов производственного назначения		
	и) обоснование схем транспортных коммуникаций, обеспечивающих внешние и внутренние (в том числе междоусебные) грузоперевозки, - для объектов производственного назначения	7	
	к) характеристика и технические показатели транспортных коммуникаций (при наличии таких коммуникаций) - для объектов производственного назначения	7	
	л) обоснование схем транспортных коммуникаций, обеспечивающих внешний и внутренний подъезд к объекту капитального строительства, - для объектов непроизводственного назначения	7	
	Приложения	8	
	Лист внесения изменений	9	
14192.012/2024-ПЗУ.ГЧ	Графическая часть	11	
Лист 1	Ситуационный план	12	
Лист 2	Схема планировочной организации земельного участка М 1:500	13	
Лист 3	Схема организации рельефа М 1:500	14	
Лист 4	План земляных масс М 1:500	15	
Лист 5	План благоустройства территории. М 1:500	16	
Лист 6	Сводный план сетей инженерно-технического обеспечения М 1:500	17	

Изм.	Кол.уч.	Лист	№ док.	Подп.	Дата

14192.016/2025-СПОЗУ

Лист

2

Текстовая часть

а) Характеристика земельного участка для размещения объекта капитального строительства

Настоящий проект разработан на основании задания на проектирование, утвержденного Заказчиком, Градостроительного плана, технических условий и следующих основных нормативных документов:

- Градостроительный кодекс РФ;
- СП 42.13330.2016 Градостроительство. Планировка и застройка городских и сельских поселений;
- СП 59.13330.2016 Доступность зданий и сооружений для маломобильных групп населения;
- СП 4.13130.2013 Системы противопожарной защиты. Ограничение распространения пожара на объекты защиты. Требования к объемно-планировочным и конструктивным решениям;
- СП 18.13330.2019 «Производственные объекты. Планировочная организация земельного участка» (СНиП П-89-80* «Генеральные планы промышленных предприятий»)
- Федеральный закон №123-ФЗ от 22.07.2008 г. «Технический регламент о требованиях пожарной безопасности»;
- ГОСТ Р 21.1101-2013 Основные требования к проектной и рабочей документации;
- Постановление Правительства РФ от 16 февраля 2008 года N 87 «О составе разделов проектной документации и требованиях к их содержанию» и т.д.;

Объект проектирования: Модернизация водоочистных сооружений в с. Салемал

Настоящим разделом предусматривается размещение здания водоочистных сооружений (поз. 1) с подключением к инженерным сетям.

Ситуационное расположение земельного участка представлено на листе 1 графической части.

Разрешенное использование земельного участка: коммунальное обслуживание (код 3.1). Участок расположен в зоне И-1 «Зона инженерной инфраструктуры».

Внешняя связь проектируемого объекта осуществляется с юго- запада с существующими проездами.

Подосновой чертежам послужила топографическая съемка (М 1:500), предоставленная заказчиком.

Система высот – Балтийская 1977 г. Система координат – условная.

Площадь земельного участка в условных границах благоустройства – 170 м².

Поверхность на участке проектирования имеет перепады высот в следствии проводимых строительных работ. Абсолютные отметки в границе проектирования изменяются от 5.2 до 6.7 в Балтийской системе высот.

						14192.016/2025-СПОЗУ. ТЧ			
Изм	Колуч	Лист	№ док.	Подп.	Дата				
Разработал		Мульдьяров			10.25	Стадия		Лист	Листов
Пров.		Петрова			10.25	П		1	6
						Текстовая часть ООО «МСБ»			
ГИП		Усвятцев			10.25				

б. Обоснование границ санитарно-защитных зон объектов капитального строительства в пределах границ земельного участка - в случае необходимости определения указанных зон в соответствии с законодательством Российской Федерации

Земельный участок полностью расположен в границах зоны с особыми условиями использования территории - водоохранная зона протоки Янгута, прибрежная защитная полоса протоки Янгута.

В границах водоохранных зон запрещаются: 1) использование сточных вод в целях регулирования плодородия почв; 2) размещение кладбищ, скотомогильников, мест захоронения отходов производства и потребления, химических, взрывчатых, токсичных, отравляющих и ядовитых веществ, пунктов захоронения радиоактивных отходов; 3) осуществление авиационных мер по борьбе с вредными организмами; 4) движение и стоянка транспортных средств (кроме специальных транспортных средств), за исключением их движения по дорогам и стоянки на дорогах и в специально оборудованных местах, имеющих твердое покрытие; 5) размещение автозаправочных станций, складов горюче-смазочных материалов (за исключением случаев, если автозаправочные станции, склады горюче-смазочных материалов размещены на территориях портов, судостроительных и судоремонтных организаций, инфраструктуры внутренних водных путей при условии соблюдения требований законодательства в области охраны окружающей среды и настоящего Кодекса), станций технического обслуживания, используемых для технического осмотра и ремонта транспортных средств, осуществление мойки транспортных средств; 6) размещение специализированных хранилищ пестицидов и агрохимикатов, применение пестицидов и агрохимикатов; 7) сброс сточных, в том числе дренажных, вод; 8) разведка и добыча общераспространенных полезных ископаемых (за исключением случаев, если разведка и добыча общераспространенных полезных ископаемых осуществляются пользователями недр, осуществляющими разведку и добычу иных видов полезных ископаемых, в границах предоставленных им в соответствии с законодательством Российской Федерации о недрах горных отводов и (или) геологических отводов на основании утвержденного технического проекта в соответствии со статьей 19.1 Закона Российской Федерации от 21 февраля 1992 года N 2395-1 "О недрах").

в. Обоснование и описание планировочной организации земельного участка в соответствии с градостроительным и техническим регламентами либо документами об использовании земельного участка (если на земельный участок не распространяется действие градостроительного регламента или в отношении его не устанавливается градостроительный регламент)

Планировочная организация земельного участка выполнена на основании утвержденного технического задания на проектирование, в соответствии с заданием на проектирование, действующими нормами, правилами, стандартами, системой проектной документации для строительства с учетом:

- границ земельного участка;
- конфигурации участка;
- объемно-планировочных решений и архитектурного облика проектируемого здания;
- соблюдение санитарных и противопожарных разрывов между зданиями.

Площадка проектируемого здания водоочистных сооружений (поз.1), представляет собой участок прямоугольной формы.

Проектируемое здание располагаются в северной части участка. Предусмотрены безопасные и комфортные пешеходные и транспортные связи, увязанные с существующими участками дорожной сети. Перемещение МГН по площадке не предусматривается.

Постоянные рабочие места в проектируемом здании не предусматриваются ввиду автоматизированных технологических процессов.

						14192.016/2025-СПОЗУ	Лист 2
Изм	Колуч	Лист	№ док	Подп	Дата		

г. Техничко-экономические показатели земельного участка, предоставленного для размещения объекта капитального строительства

В границах отвода участка

№ п/п	Наименование	Ед. изм.	Количе- ство	Примечание
1	Площадь земельного участка в условных границах благоустройства	м ²	170	
2	Площадь застройки проектируемая застройка (поз. 1)	м ²	39,3	
3	Площадь проектируемых твердых покрытий	м ²	96	

**д. Обоснование и описание решений по инженерной подготовке территории, в том числе решений по инженерной защите территории и объектов капитального строительства от последствий опасных геологических процессов, паводковых, поверхностных и грунто-
вых вод**

С целью предотвращения эрозионных процессов и для закрепления грунта предусмотрены следующие мероприятия:

- устройство щебеночного покрытия площадки, предотвращающее проникновение загрязнений в почву и подпочвенные воды.

Заболоченность отсутствует. Площадка очистных сооружений находится в насыпи.

е. Описание организации рельефа вертикальной планировкой

Проектом решаются вопросы вертикальной посадки зданий и сооружений, планировки территории, отвода ливневых и талых вод.

Вертикальная планировка выполнена исходя из условий существующего расположения здания доочистки, в увязке с отметками прилегающего существующего проезда, удобного и безопасного движения транспортных средств и пешеходов, беспрепятственного водоотвода, что достигается необходимыми продольными и поперечными уклонами поверхности.

Поверхность на участке проектирования относительно ровная с плавным понижением в восточном направлении. Абсолютные отметки в границе проектирования изменяются от 5.2 до 6.7 в Балтийской системе высот.

План организации рельефа выполнен методом проектных отметок. Планировка поверхности производится только на месте размещения проектируемого здания.

Продольные уклоны проездов по площадке проектирования приняты согласно действующих нормативов и составляют 5-10‰.

ж. Описание решений по благоустройству территории

Проектом предусматривается благоустройство территории проектируемого здания водоочистных сооружений (поз. 1)

По периметру предусмотрена площадка с щебеночным покрытием. Подъезд к проектируемому зданию осуществляется по существующему твердому покрытию.

Покрытие отмостки – бетонное.

						14192.016/2025-СПОЗУ	Лист
							3
Изм	Колуч	Лист	№ док.	Подп.	Дата		

Проектируемый объект обеспечен удобными транспортно-пешеходными связями.
Все ведомости по благоустройству территории представлены на листе 5 графической части.
Для объекта парковка не предусматривается, т.к., в проектируемом здании постоянных рабочих мест нет.

Контейнер ТБО

Для временного хранения отходов имеется площадка с контейнером для ТБО.

з. Обоснование зонирования территории земельного участка, предназначенного для размещения объекта капитального строительства, а также принципиальная схема размещения территориальных зон с указанием сведений о расстояниях до ближайших установленных территориальных зон и мест размещения существующих и проектируемых зданий, строений и сооружений (основного, вспомогательного, подсобного, складского и обслуживающего назначения) объектов капитального строительства - для объектов производственного назначения

Зонирование территории, на которой расположен проектируемый объект не предполагается.

и. Обоснование схем транспортных коммуникаций, обеспечивающих внешние и внутренние (в том числе межцеховые) грузоперевозки, - для объектов производственного назначения

К проектируемому зданию существует подъезды. Сеть существующих и проектируемых проездов обеспечивает технологические и противопожарные подъезды и проезды к зданиям.

к. Характеристика и технические показатели транспортных коммуникаций (при наличии таких коммуникаций) - для объектов производственного назначения

К площадке проектируемого здания водоочистных сооружений предусматривается подвод внешних инженерных сетей, в том числе: сети электроснабжение, водопровод, канализация, сети связи.

Инженерные сети прокладываются подземным способом.

л. Обоснование схем транспортных коммуникаций, обеспечивающих внешний и внутренний подъезд к объекту капитального строительства, - для объектов непроизводственного назначения

Рассматриваемы проектом объект относится к производственным.

						14192.016/2025-СПОЗУ	Лист
							4
Изм	Колуч	Лист	№ док	Подп	Дата		

ПРИЛОЖЕНИЯ

[illegible]


						14192.016/2025-СПОЗУ	Лист
							6
Изм	Копуч	Лист	№ док.	Подп.	Дата		

ГРАФИЧЕСКАЯ ЧАСТЬ


Инв. № подл.	Подп. и дата	Взам. инв. №



						14192.016/2025-СПОЗУ			
						Модернизация водоочистных сооружений в с. Салемал			
Изм.	Кол. уч.	Лист	№ док.	Подп.	Дата	Схема планировочной организации земельного участка	Стадия	Лист	Листов
Разработал		Мульдияров			10.25		П	1	3
Проверил		Усвяцев			10.25				
Н.контр.		Шамова			10.25	Ситуационный план	ООО "МСБ"		
ГИП		Усвяцев			10.25				

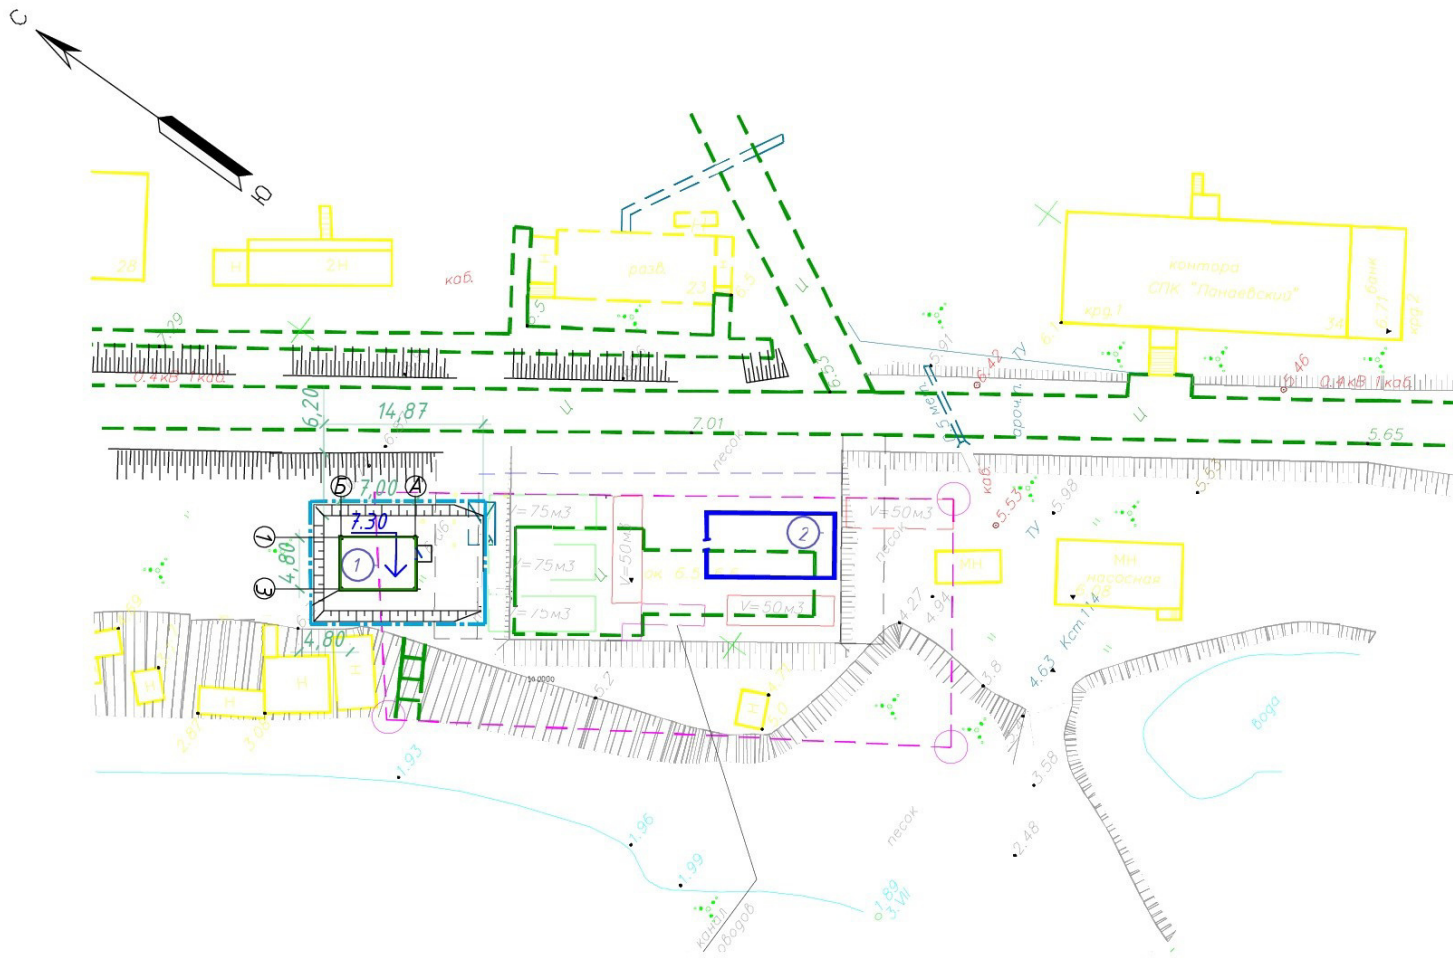

Условные обозначения

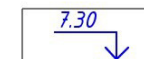

Отметка ноля проектируемого здания



Условная граница производства работ

Все размеры даны в метрах.

Экспликация зданий и сооружений

N поз.	Наименование	Примечание
1	Здание водоочистных сооружений	Проект.
2	Здание ВОС	Сущ.

						14192.016/2025-СПОЗУ			
						Модернизация водоочистных сооружений в с. Салемал			
Изм.	Кол. уч	Лист	№ док.	Подп.	Дата	Схема планировочной организации земельного участка	Стадия	Лист	Листов
Разработал	Мульдияров				10.25		П	2	3
Проверил	Усвьяцев				10.25	Схема планировочной организации земельного участка М 1:500	ООО "МСБ"		
Н.контр.	Шамова				10.25				
ГИП	Усвьяцев				10.25				

