




Условные обозначения трубопроводов и потоков:	
—	B10 Трубопровод исходной воды
—	B20 Трубопровод от контактных колонн к фильтрам I ступени
—	B30 Трубопровод отфильтрованных вод к фильтрам II ступени
—	B40 Трубопровод отфильтрованных вод к фильтрам III ступени
—	B50 Трубопровод обеззараживания и подачи к потребителю
—	B60H Напорный трубопровод чистой промывной воды
—	B70 Трубопровод собственных нужд
—	B80 Трубопровод отбора проб
—	K10 Отвод первого фильтрата
—	K20H Напорный трубопровод грязной промывной воды
—	K30 Канализация собственных нужд
—	P1 Трубопровод гипохлорита натрия
—	P2 Трубопровод коагулянта
—	P3 Трубопровод щёлочи
—	P4 Трубопровод флокулянта
—	B90 Трубопровод системы механической очистки "Гидроциклон"

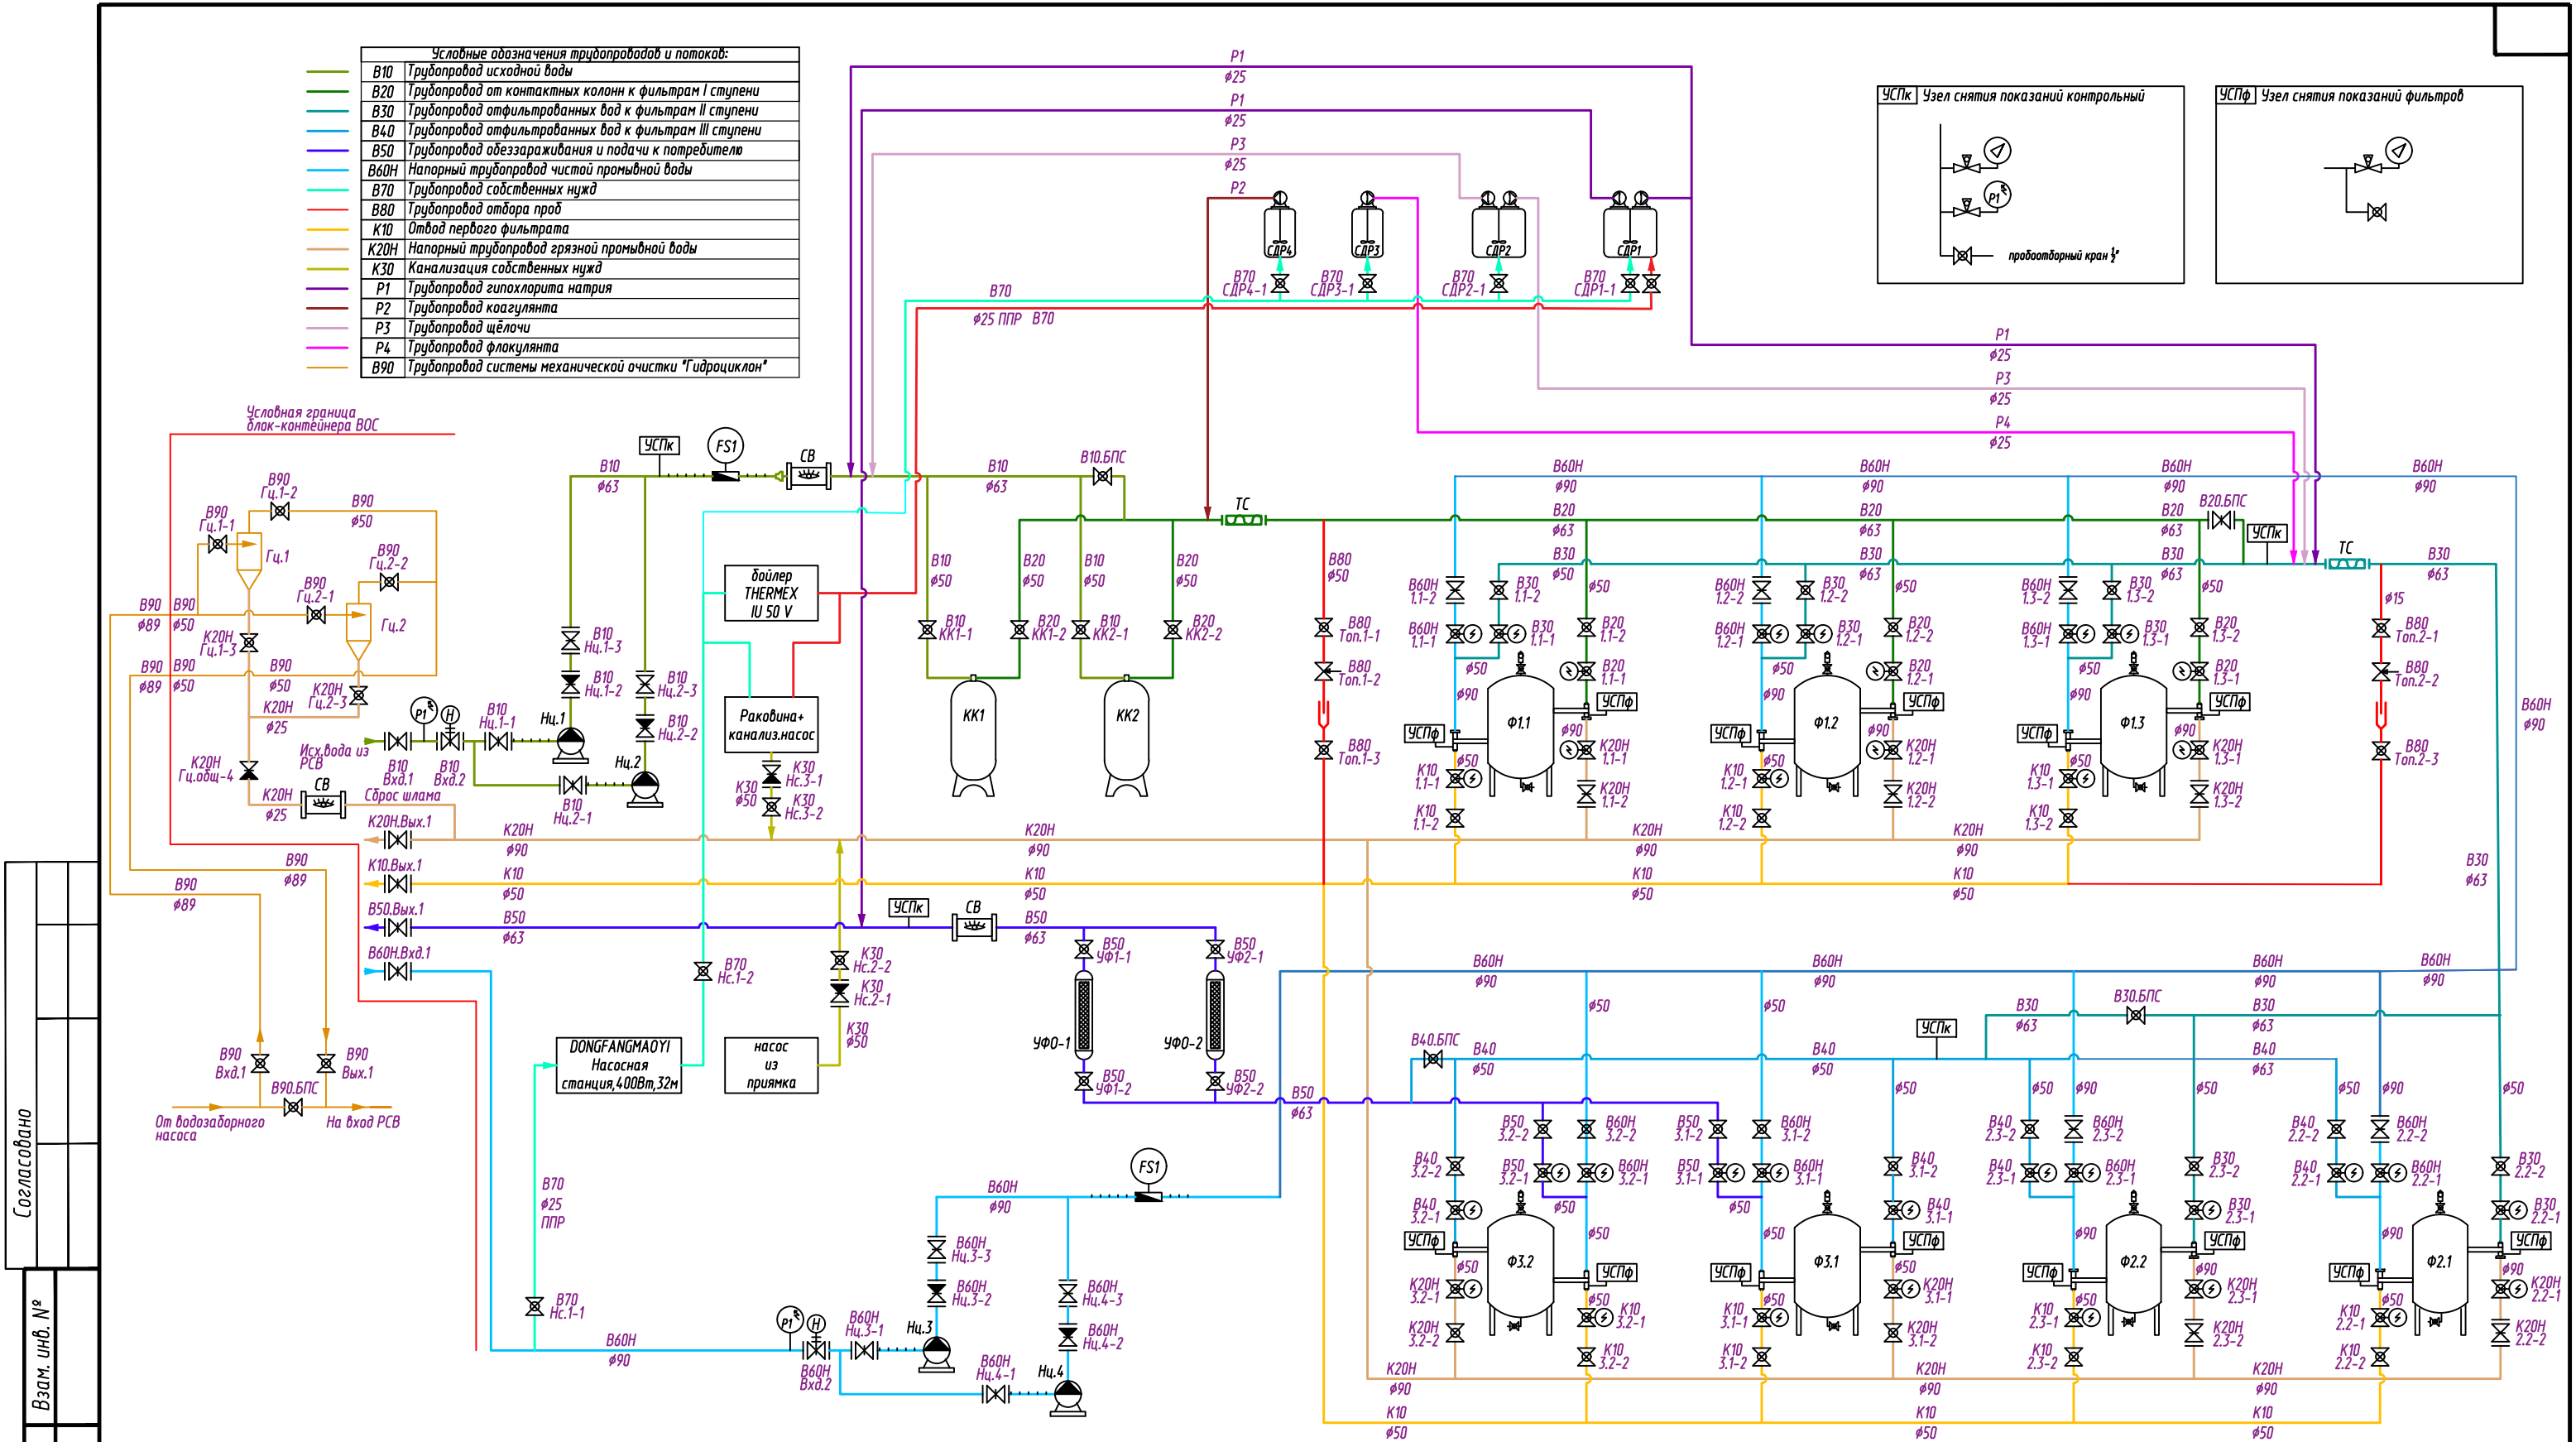

Согласовано				
Взам. инв. №				
Подп. и дата				
Инв. № подл.				

Условное графическое обозначение

	Затвор дисковый с электроприводом		Кран шаровый с электроприводом		Расходомер
	Затвор дисковый		Кран шаровый		Насос центробежный
	Обратный клапан		Кран игольчатый		Смеситель статический
	Манометр электронный		Кран для манометра		Смотровое окно
	Манометр показывающий				

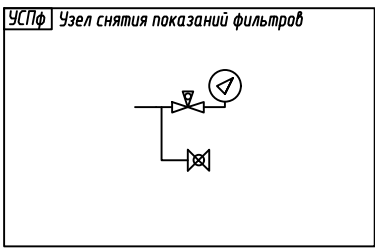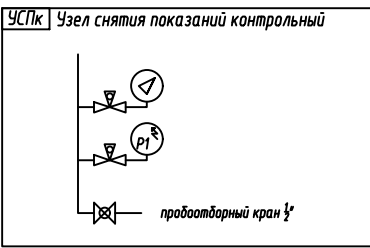

Изм.	Кол.уч.	Лист.	Ндок.	Подпись	Дата				
Разработал	ФИО 1				12.05.25	Стадия	Лист	Листов	
Проверил	ФИО 2				12.05.25				
Н.контр.	ФИО 3				12.05.25				